




PROJECT: CLIENT: SITE LOCATION: DATE: STATUS: SITE VERIFICATION

DWG 01-PLN 2D ARCHITECTURAL FLOOR PLAN & OVERALL SPACE LAYOUT

SCALE: 1:50 • PLAN VIEW • ALL DIMS BLANK FOR SITE ENTRY

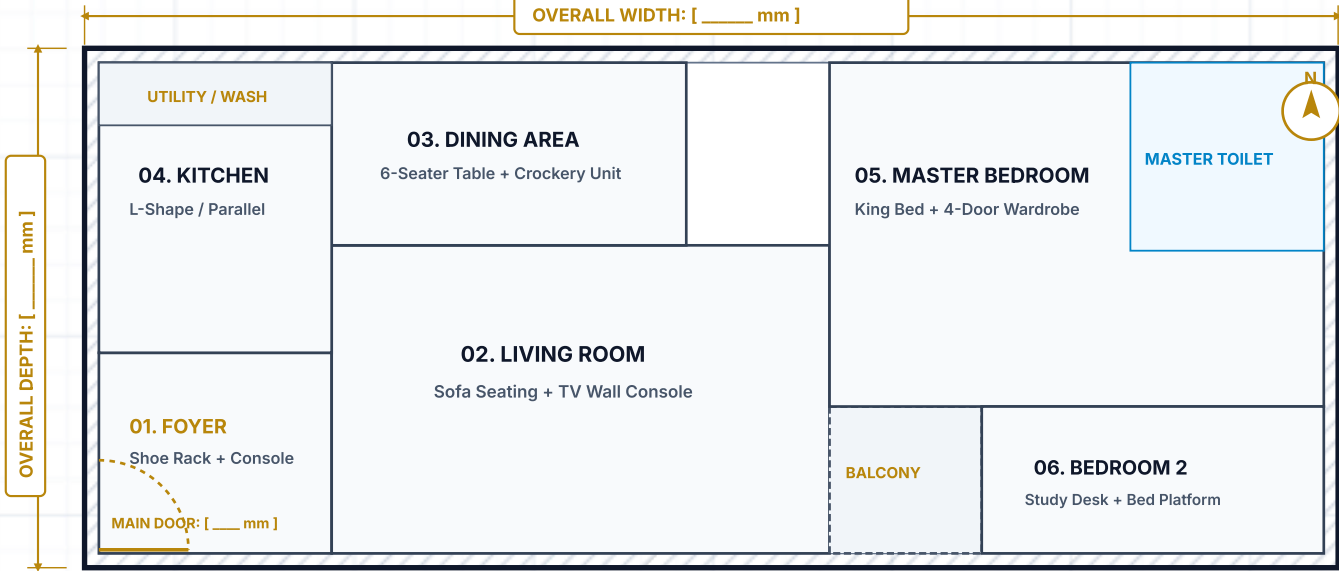

FOYER: W: x D:

LIVING: W: x D:

MASTER BED: W: x D:

01 CLIENT IDENTIFICATION

Project Name:
Client Name:
Studio Helpline: +91 93805 23743
Client Contact:
Site Location / Unit:

REMARKS:

02 PROJECT SPECIFICATIONS

PROPERTY TYPE:
☐ Apartment ☐ Villa / Row House
☐ Independent House ☐ Commercial / Office

Expected Handover Date: DD / MM / YYYY
Design Theme Preference: Modern / Contemporary / Japandi
Key Project Milestones: Civil → Modular → Painting → Handover

REMARKS:



PROJECT: _____

CLIENT: _____


SITE LOCATION: _____

DATE: _____

STATUS: SITE VERIFICATION

DWG 02-CIV CIVIL LAYOUT, COLUMN GRID & STRUCTURAL MODIFICATION PLAN

SCALE: 1:50 • STRUCTURAL PLAN • ALL DIMS BLANK FOR SITE ENTRY

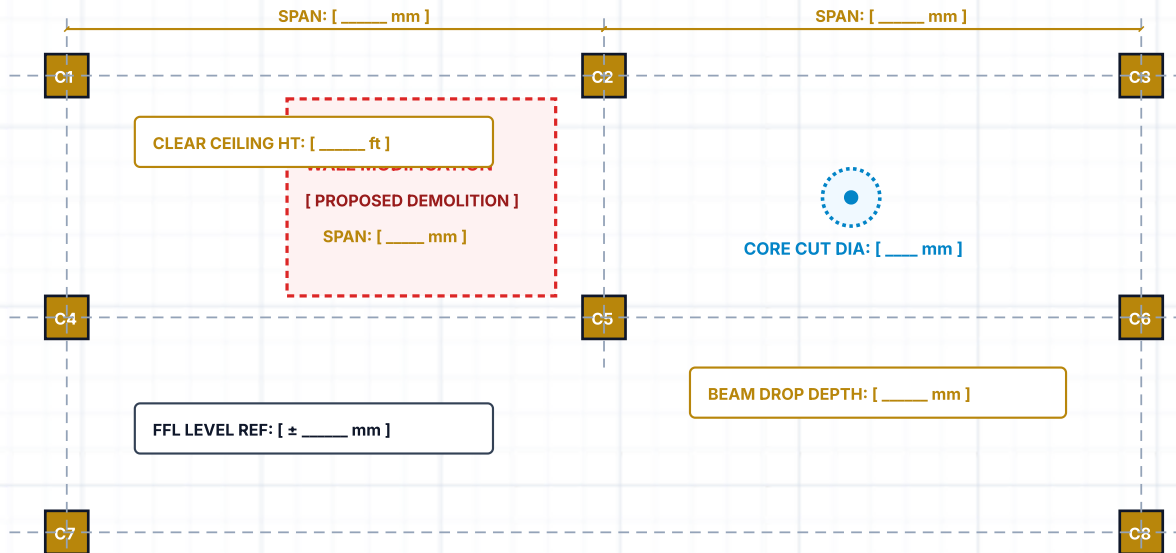

01 DIMENSIONS & CONFIGURATION

Total Built-up Area: _____ sq.ft. Carpet Area: _____ sq.ft.

UNIT CONFIGURATION:

☐ 1 BHK / 2 BHK☐ 3 BHK / 4 BHK☐ Duplex / Penthouse☐ Studio / Custom

No. of Floors: _____

Clear Ceiling Height: _____ ft.

REMARKS: _____

02 CIVIL & STRUCTURAL WORK

PROPOSED CIVIL / STRUCTURAL WORK:

☐ Wall Demolition☐ New Drywall Partition☐ Plumbing Core Cut☐ Door Frame Shift

Civil Details / Scope: _____

Structural Check: _____

REMARKS: _____



PROJECT: _____

CLIENT: _____

SITE LOCATION: _____

DATE: _____

STATUS: SITE VERIFICATION

DWG 03-MAT

ARCHITECTURAL MATERIAL PALETTE & JOINERY PROFILES

SCALE: 1:2 • TECHNICAL DETAIL SECTIONS • ALL DIMS BLANK FOR SITE ENTRY

A. ACOUSTIC FLUTED PANEL DETAIL



SLAT WIDTH: [____ mm]

SLAT DEPTH: [____ mm]

12mm MDF Substrate + 0.8mm Natural Veneer

B. STONE COUNTERTOP EDGE PROFILE



THICKNESS: [____ mm]

CHAMFER RADIUS: [____ mm]

Quartz / Italian Marble / Granite

C. BRASS PVD T-PROFILE TRIM



FLANGE: [____ mm]

INSERT STEM: [____ mm]

Rose Gold / Brushed Brass / Matt Black

D. SLIMLINE GLASS FRAME PROFILE



FRAME WIDTH: [____ mm]

GLASS THICKNESS: [____ mm]

Fluted / Tinted Grey / Toughened

01 THEME & COLOR PALETTE

PRIMARY INTERIOR DESIGN THEME:

- ☐ Modern Minimal ☐ Contemporary
☐ Japandi / Wabi-Sabi ☐ Neo-Classical

COLOR PALETTE DIRECTION:

- ☐ Warm Neutrals & Beige ☐ Moody Dark Slate
☐ Earthy Sage & Ochre ☐ Monochrome Tone

REMARKS: _____

02 MATERIAL FINISH SELECTIONS

KEY JOINERY & SURFACE FINISHES:

- ☐ Natural Teak/Walnut Veneer ☐ High-Gloss Acrylic
☐ Matte PU Paint Finish ☐ Fluted Acoustic Slats

Inspiration Link: Pinterest / Drive / Portfolio LinkMoodboard Sign-off: DD / MM / YYYY

REMARKS: _____





PROJECT:

CLIENT:


SITE LOCATION:

DATE:

STATUS: SITE VERIFICATION

DWG 04-ELV LIVING ROOM TV UNIT & FEATURE WALL ELEVATION

SCALE: 1:25 • 2D FRONT ELEVATION • ALL DIMS BLANK FOR SITE ENTRY

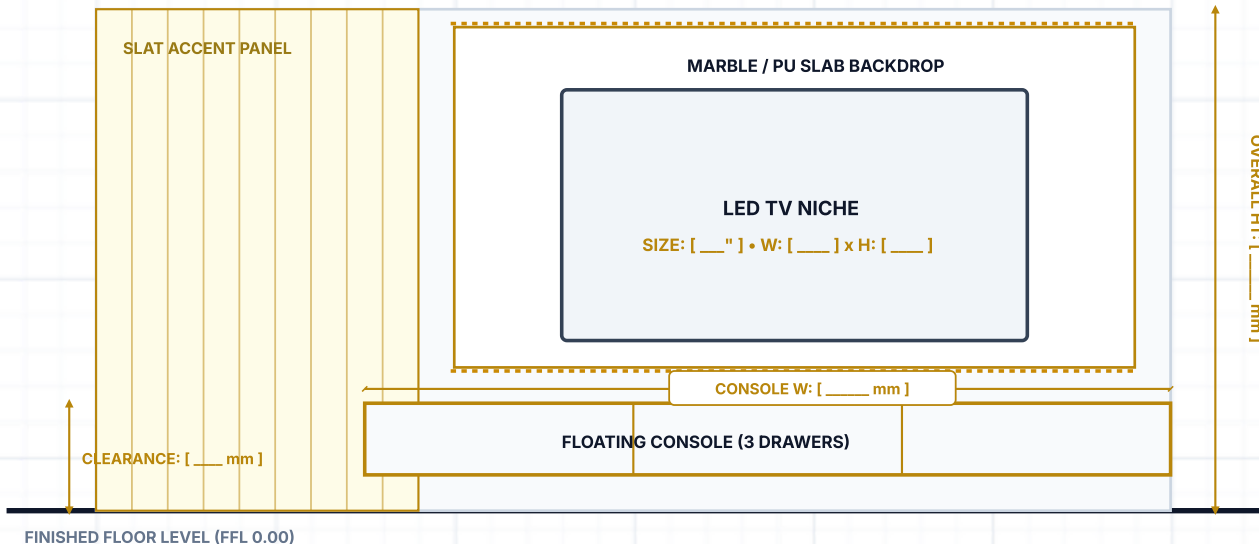

01 FURNITURE & CEILING

TV CONSOLE UNIT STYLE:

- | | |
|---|---|
| ☐ Floating Wall Credenza | ☐ Floor Standing Console |
| ☐ Full Paneling Feature Wall | ☐ Built-in LED TV Niche |

SOFA & SEATING LAYOUT:

- | | |
|--|--|
| ☐ L-Shaped Sectional | ☐ 3 + 2 + 1 Seater Set |
| ☐ Recliner Lounger Unit | ☐ Accent Armchairs (Pair) |

CEILING TREATMENT:

- | | |
|---|---|
| ☐ Perimeter Cove Light | ☐ Center Floating Island |
|---|---|

REMARKS:

02 WALL FINISHES & LIGHTING

FEATURE WALL & BACKDROP PANELING:

- | | |
|--|---|
| ☐ Acoustic Fluted Slats | ☐ Bookmatched Marble Slab |
| ☐ Designer Themed Wallpaper | ☐ PU Textured Paint Finish |

ARCHITECTURAL LIGHTING:

- | | |
|--|---|
| ☐ Warm 3000K Cove Strip | ☐ Anti-Glare COB Spots |
| ☐ Magnetic Track Light Rail | ☐ Chandelier Center Drop |

Window Treatments: Motorized 100% Blackout Drapes + Sheer Curtai...

REMARKS:





PROJECT: _____

CLIENT: _____


SITE LOCATION: _____

DATE: _____

STATUS: SITE VERIFICATION

DWG 05-ELV DINING TABLE & CROCKERY UNIT 2D ELEVATION

SCALE: 1:25 • 2D ELEVATION • ALL DIMS BLANK FOR SITE ENTRY

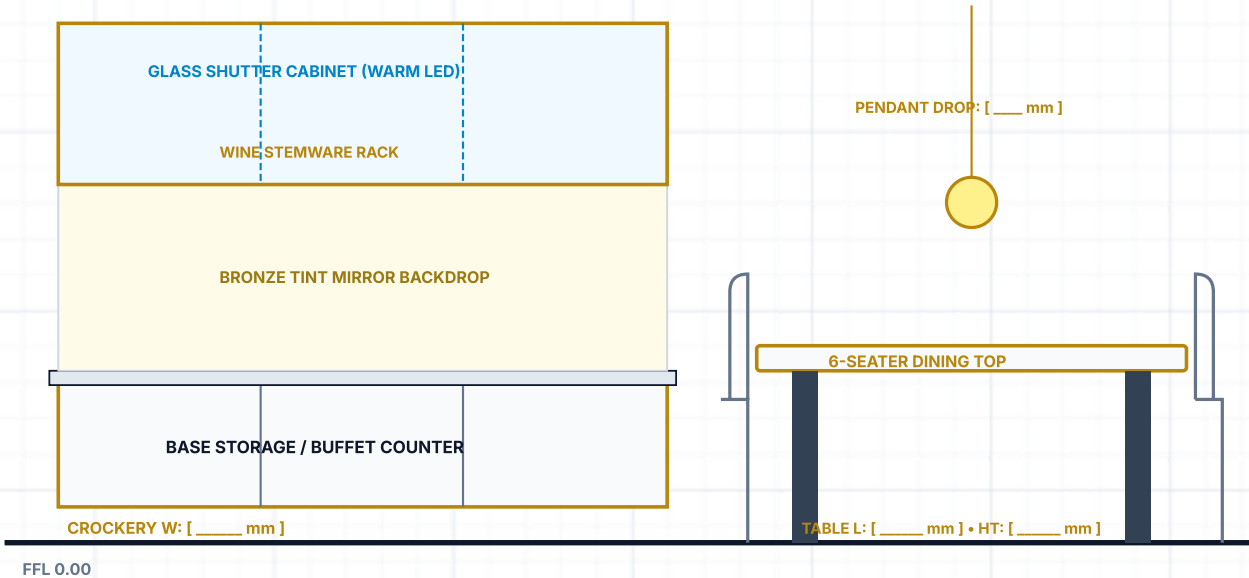

01 DINING TABLE & SEATING

DINING TABLE SEATING:

- ☐ 4-Seater Compact ☐ 6-Seater Standard
☐ 8-Seater Extended ☐ Extendable Mechanism

TABLETOP SLAB MATERIAL:

- ☐ Italian Onyx / Marble ☐ Sintered Stone / Quartz
☐ Solid Teak Wood Top ☐ Tinted Toughened Glass

CROCKERY UNIT STYLE:

- ☐ Full-Height with Loft ☐ Floating Buffet Ledge

REMARKS: _____

02 CROCKERY UNIT & AMBIENCE

CROCKERY CABINET SPECIFICATIONS:

- ☐ Slim Aluminium Profile ☐ Fluted Tinted Glass
☐ Warm LED Strip Shelves ☐ Wine Stemware Rack

NICHE BACKDROP TREATMENT:

- ☐ Tinted Bronze Mirror ☐ Fluted Wooden Slats

Pendant Drop Clearance: 750 - 850 mm above dining tabletop

Bar Counter Integration: Compact Service Counter + Wine Rack (Yes / ...)

REMARKS: _____



PROJECT:

CLIENT:


SITE LOCATION:

DATE:

STATUS: SITE VERIFICATION

DWG 06-KIT MODULAR KITCHEN CARCASS & ERGONOMIC ELEVATION

SCALE: 1:25 • 2D WALL ELEVATION • ALL DIMS BLANK FOR SITE ENTRY

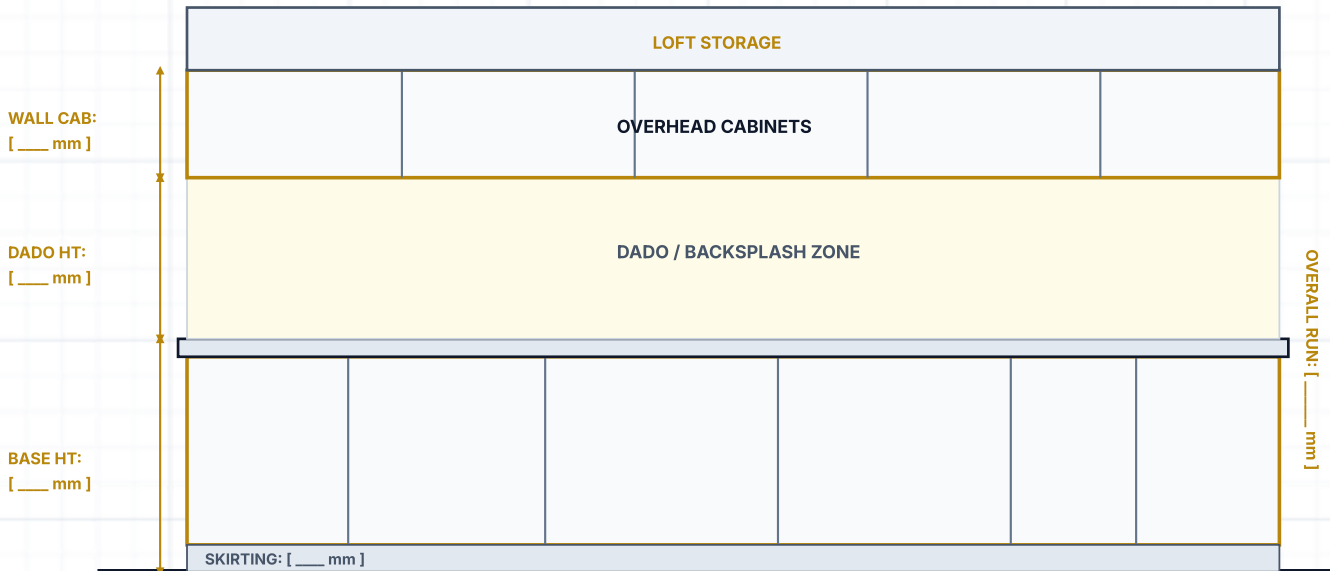

01 LAYOUT & CARCASS CORE

KITCHEN LAYOUT TYPE:

- ☐ Straight Run ☐ L-Shaped Layout
☐ U-Shaped Layout ☐ Parallel / Galley

KITCHEN ENCLOSURE:

- ☐ Open Concept Kitchen ☐ Closed Partition
☐ Glass Sliding Partition ☐ Breakfast Counter

CARCASS CORE MATERIAL:

- ☐ BWP Marine Plywood (IS:710) ☐ BWR Grade Plywood

REMARKS:

02 SHUTTER & COUNTER FINISH

SHUTTER SURFACE FINISH:

- ☐ Anti-Fingerprint Acrylic ☐ Matte PU Paint Finish
☐ 1mm Merino Laminate ☐ Ceramic / Slim Glass

COUNTERTOP STONE SELECTION:

- ☐ Composite Quartz (15-20mm) ☐ Black Granite
☐ Nano White Top ☐ Full-Body Vitrified

Backsplash Dado Material: Vitrified Slab / Lacquered Glass / Subway ...

REMARKS:



PROJECT: _____

CLIENT: _____

SITE LOCATION: _____

DATE: _____

STATUS: **SITE VERIFICATION**

DWG 07-ACC KITCHEN STORAGE HARDWARE & ACCESSORIES DETAIL

SCALE: 1:15 • INTERNAL SECTION ELEVATION • ALL DIMS BLANK FOR SITE ENTRY

1. DRAWER STACK

CUTLERY TRAY ORGANIZER

HT: [____ mm]

CUP & SAUCER TANDEM

HT: [____ mm]

THALI / POT TANDEM

HT: [____ mm]

2. CORNER SOLUTION

MAGIC CORNER /
LeMANS SWING TRAY

SHUTTER W: [____ mm]

Soft-close Hydraulic Blind Corner

3. TALL PANTRY UNIT

6-TIER WIRE / SOLID BASKET

WIDTH: [____ mm]

HEIGHT: [____ mm]

01 DRAWER STACKS & CORNER UNITS

DRAWER HARDWARE SYSTEMS:

- | | |
|--|---|
| ☐ Blum Tandembox / Antaro | ☐ Hettich InnoTech Atira |
| ☐ Hafele Matrix Box | ☐ Soft-Close Telescopic |

DRAWER ORGANIZERS:

- | | |
|---|--|
| ☐ Cutlery Tray Organizer | ☐ Cup & Saucer Basket |
| ☐ Thali & Pot Organizer | ☐ Plate Stacker Unit |

BLIND CORNER UNITS:

- | | |
|--|--|
| ☐ LeMans II Swing Trays | ☐ Magic Corner S-Carousel |
| ☐ Lazy Susan Carousel | ☐ Corner Shelf Ledges |

REMARKS: _____

02 PULL-OUTS & PANTRY STORAGE

PULL-OUT UNITS & ACCESSORIES:

- | | |
|--|--|
| ☐ 150/200mm Spice Pull-out | ☐ Under-sink Detergent Rack |
| ☐ Double Waste Bin Pull-out | ☐ Tall Pantry (6 Baskets) |
| ☐ Wicker Vegetable Baskets | ☐ Appliance Roller Shutter |

Hardware Load Rating: Blum / Hettich 30-50 kg Dynamic Load Tested


Warranty Terms: 10 Years Carcass + Lifetime Soft-Close Runners

REMARKS: _____

PROJECT: _____ CLIENT: _____ SITE LOCATION: _____ DATE: _____ STATUS: **SITE VERIFICATION**

DWG 08-APP KITCHEN BUILT-IN APPLIANCES & FIXTURE INTEGRATION

SCALE: 1:20 • 2D ELEVATION • ALL DIMS BLANK FOR SITE ENTRY

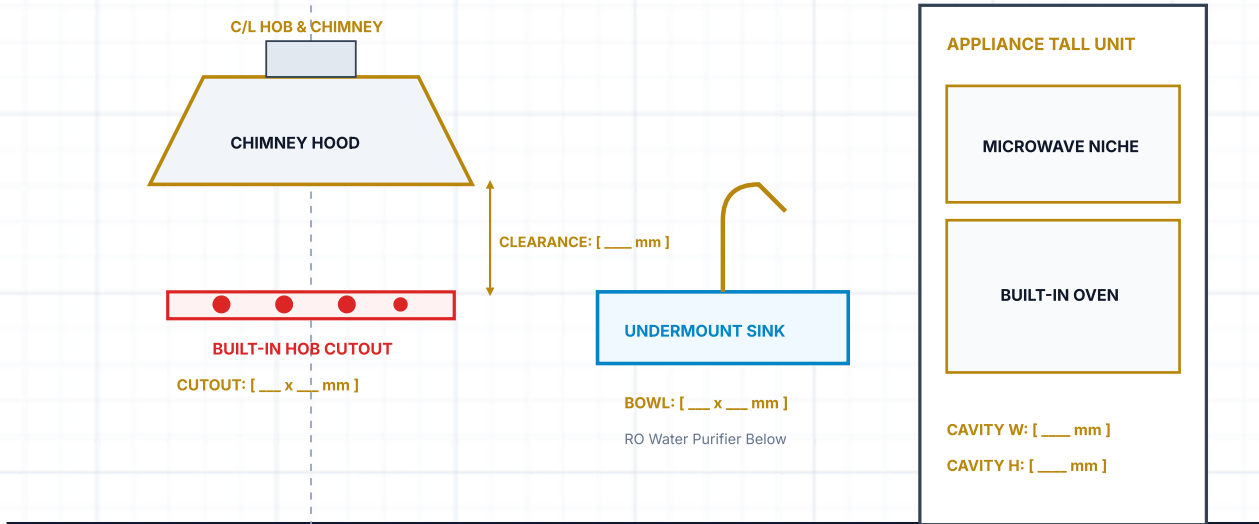

01 SINK, HOB & CHIMNEY FIXTURES

KITCHEN SINK & FAUCET:

- | | |
|--|---|
| ☐ Quartz Composite Sink | ☐ SS 304 Undermount Sink |
| ☐ Single Bowl with Drainer | ☐ Double Bowl Sink |
| ☐ Pull-out Swivel Spray Tap | ☐ RO Integrated Faucet |

COOKING HOB & CHIMNEY:

- | | |
|---|--|
| ☐ 3-Burner Gas Glass Hob | ☐ 4-Burner Built-in Hob |
| ☐ Induction Cooktop | ☐ Filterless Autoclean Hood |

REMARKS: _____

02 BUILT-IN APPLIANCES & UTILITIES

BUILT-IN TALL APPLIANCES:

- | | |
|---|--|
| ☐ Built-in Microwave (25L) | ☐ Built-in Oven (60L) |
| ☐ Dishwasher (12-14 Place) | ☐ Built-in Refrigerator |

UTILITY PROVISIONS:

- | | |
|--|---|
| ☐ RO Water Purifier Inlet | ☐ Dedicated 15L Geyser |
|--|---|

Dedicated 16A Outlets: Chimney, Microwave, Oven, Refrigerator, RO, ...

REMARKS: _____



PROJECT: _____

CLIENT: _____


SITE LOCATION: _____

DATE: _____

STATUS: SITE VERIFICATION

DWG 09-BED MASTER BEDROOM BED WALL & NIGHTSTAND ELEVATION

SCALE: 1:25 • 2D ELEVATION • ALL DIMS BLANK FOR SITE ENTRY

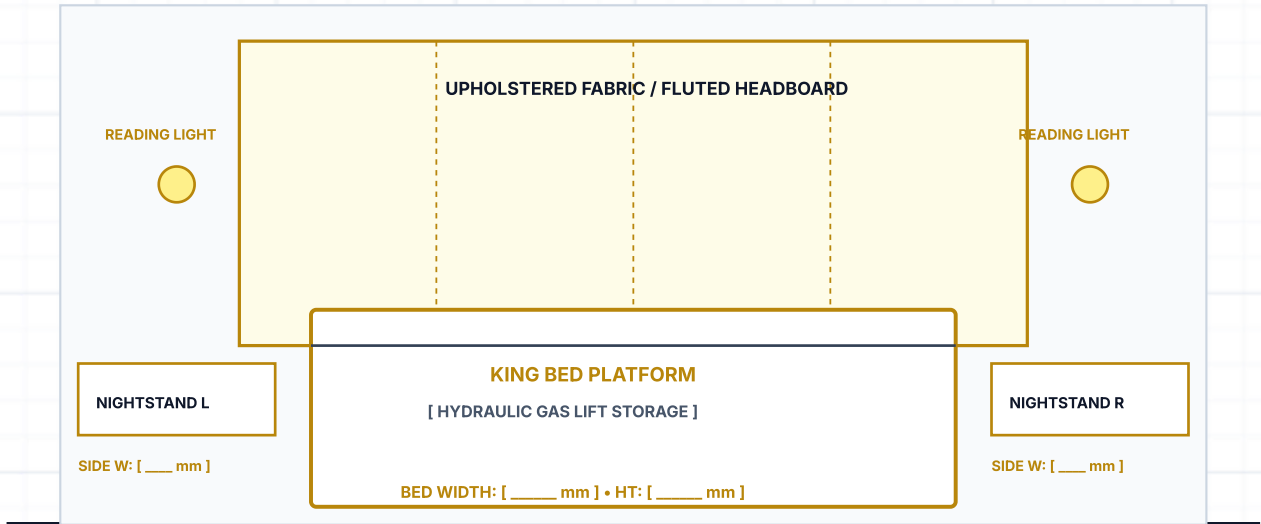

01 BED & HEADBOARD SPECIFICATIONS

BED PLATFORM CONFIGURATION:

- ☐ King Size (72" x 78") ☐ Queen Size (60" x 78")
☐ Hydraulic Gas Lift Storage ☐ Side Pull-out Drawers

HEADBOARD WALL DESIGN:

- ☐ Fluted Wooden Paneling ☐ Upholstered Velvet Fabric
☐ Matte PU Paint Finish ☐ Integrated LED Backlight

REMARKS: _____

02 SIDE TABLES, DRESSER & LIGHTING

BEDSIDE, DRESSER & LIGHTING:

- ☐ Dual Floating Nightstands ☐ Floor Pedestal (2 Drawers)
☐ Full-Length Dressing Mirror ☐ Floating Vanity with LED
☐ Bedside 2-Way Switches ☐ Directional Reading Spots

Master Window Treatments: 100% Blackout Motorized Curtains + She...

REMARKS: _____



PROJECT: _____

CLIENT: _____

SITE LOCATION: _____


DATE: _____

STATUS: **SITE VERIFICATION**

DWG 10-KID

BEDROOM 2 INTEGRATED STUDY DESK & BED ELEVATION

SCALE: 1:25 • 2D ELEVATION • ALL DIMS BLANK FOR SITE ENTRY

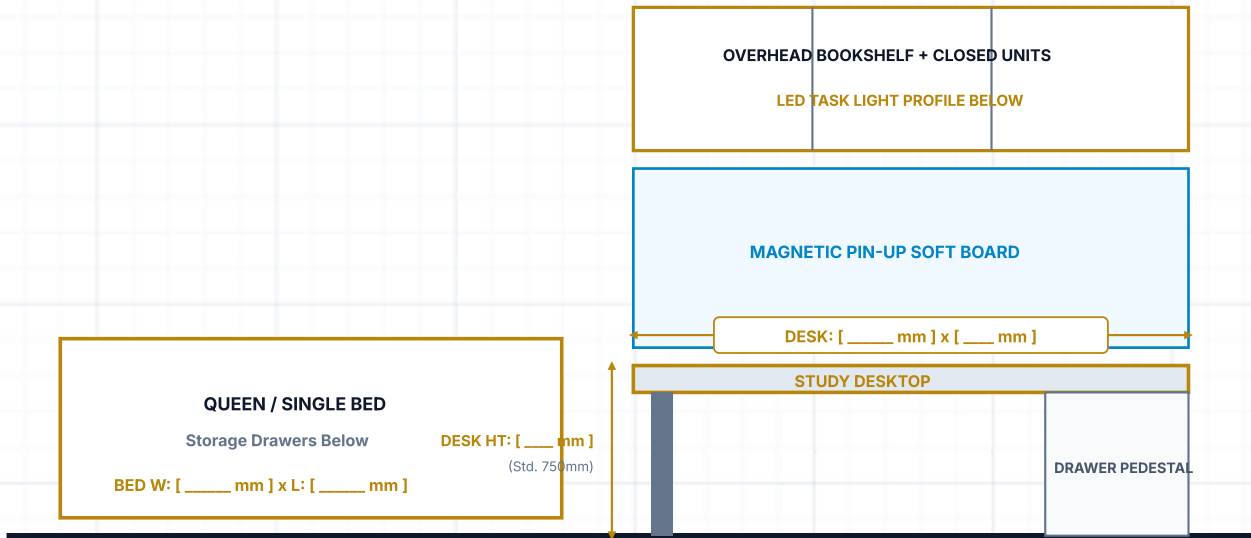

01 ROOM USE, BED & STUDY DESK

ROOM PURPOSE & BED SELECTION:

- | | |
|--|--|
| ☐ Kids Bedroom | ☐ Guest Bedroom |
| ☐ Parents / Senior Room | ☐ Home Office / Study |
| ☐ Queen Size Bed | ☐ Single Bed with Trundle |

STUDY DESK STYLE:

- | | |
|---|---|
| ☐ Wall-Mounted Ledge | ☐ Pedestal Desk with Drawers |
|---|---|

REMARKS: _____

02 BOOKSHELF & ELECTRICAL SPECIFICATIONS

OVERHEAD BOOKSHELF & WALL ACCENT:

- | | |
|--|---|
| ☐ Open Bookshelf Compartments | ☐ Closed Shutter Cabinets |
| ☐ Magnetic Soft Pin-up Board | ☐ Under-shelf Task LED Strip |
| ☐ Designer Themed Wallpaper | ☐ Accent Color Wall Paint |

Desk Dimensions: L: [_____ mm] x D: [_____ mm]

Cable Management: Desk Grommet Hole + 4-Plug Power Sockets

REMARKS: _____




PROJECT: CLIENT: SITE LOCATION: DATE: STATUS: SITE VERIFICATION

DWG 11-WAR

WARDROBE INTERNAL CARCASS & SHELF CONFIGURATION

SCALE: 1:25 • INTERNAL SECTIONAL ELEVATION • ALL DIMS BLANK FOR SITE ENTRY

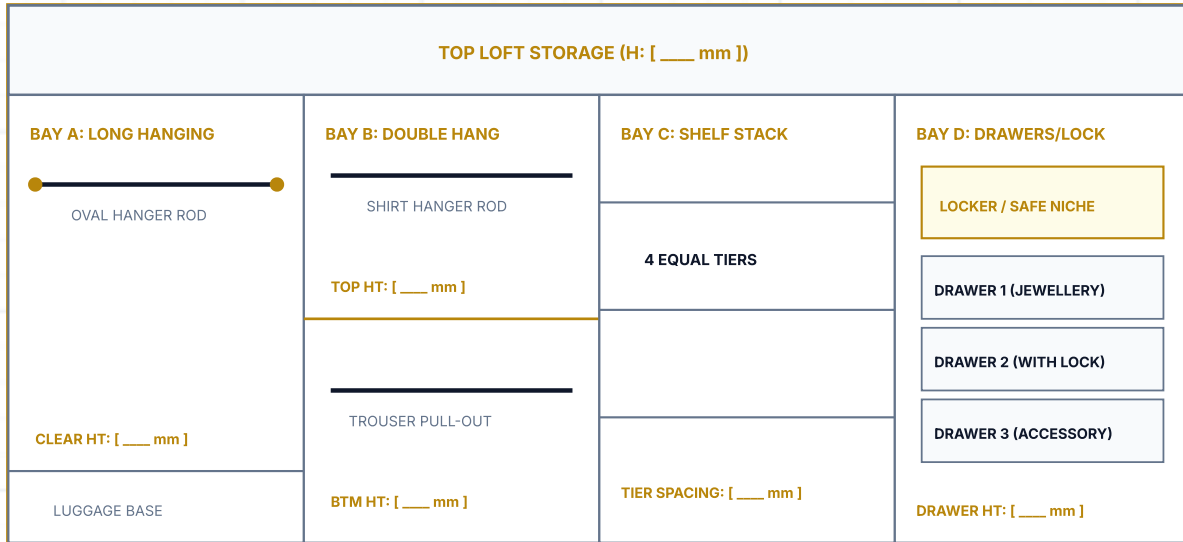

01 CARCASS SPECIFICATIONS & LOFT

WARDROBE CARCASS & LAYOUT:

- ☐ Straight 3-Door ☐ Straight 4-Door
☐ L-Shaped Corner ☐ Walk-in Closet Suite

CARCASS CORE & LOFT:

- ☐ 18mm BWP Marine Plywood ☐ 18mm HDHMR Board
☐ Full-Height Seamless to Ceiling ☐ Independent Loft Shutters

REMARKS:

02 INTERNAL HANGING & DRAWER BAYS

INTERNAL SECTION ALLOCATION:

- ☐ Bay A: Long Coat Hanging Rod ☐ Bay B: Double Shirt Hanging Rods
☐ Bay C: 4-Tier Folded Shelves ☐ Bay D: 3 Internal Drawers

Internal Locker / Safe Niche: Reinforced Compartment with Digital Nu...

Internal Shutter Finish: 0.8mm Off-White Liner / Fabric Texture Lamin...


REMARKS:



PROJECT: _____ CLIENT: _____ SITE LOCATION: _____ DATE: _____ STATUS: SITE VERIFICATION

DWG 12-HRD WARDROBE SHUTTERS, PROFILE HANDLES & HARDWARE DETAIL

SCALE: 1:25 • EXTERIOR ELEVATION • ALL DIMS BLANK FOR SITE ENTRY

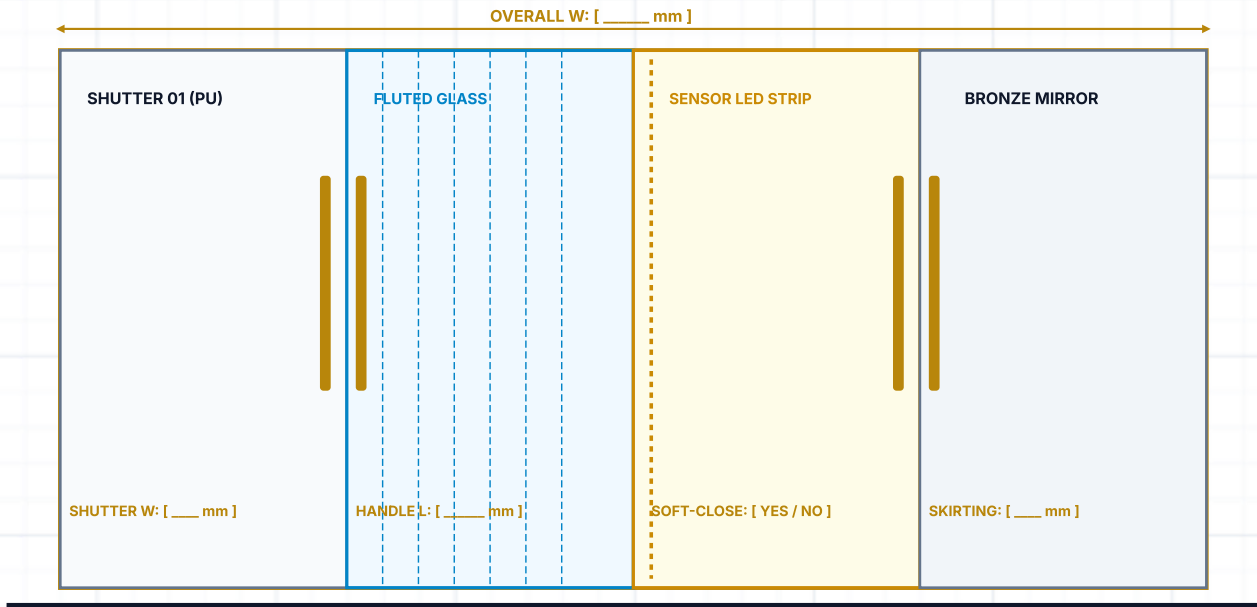

01 SHUTTER MECHANISM & FINISH

SHUTTER DOOR MECHANISM:

- ☐
- Hinged Openable Doors
- ☐
- Sliding Doors (Top-Hung)

EXTERIOR SHUTTER FINISH:

- ☐
- Matte PU Paint Finish
- ☐
- High-Gloss Acrylic
-
- ☐
- 1mm Textured Laminate
- ☐
- Tinted Bronze Mirror
-
- ☐
- Fluted Glass in Alu Frame
- ☐
- Natural Wood Veneer

REMARKS: _____

02 HANDLES & PULL-OUT ACCESSORIES

HARDWARE & ACCESSORIES:

- ☐
- Full-Height Gola Profile Handle
- ☐
- Knurled Brass Handles
-
- ☐
- Push-to-Open Latches
- ☐
- Trouser Hanger Rack
-
- ☐
- Tie & Belt Pull-out
- ☐
- Automatic Sensor LED Strip

Hardware Finish Tone: Brushed Brass Gold / Matt Black / Satin NickelSoft-Close Hinges Brand: Blum Clip-Top BLUMOTION / Hettich Sensy...

REMARKS: _____



PROJECT: _____

CLIENT: _____

SITE LOCATION: _____


DATE: _____

STATUS: SITE VERIFICATION

DWG 13-SAN

WASHROOM VANITY COUNTER & BASIN DETAIL ELEVATION

SCALE: 1:20 • 2D ELEVATION • ALL DIMS BLANK FOR SITE ENTRY

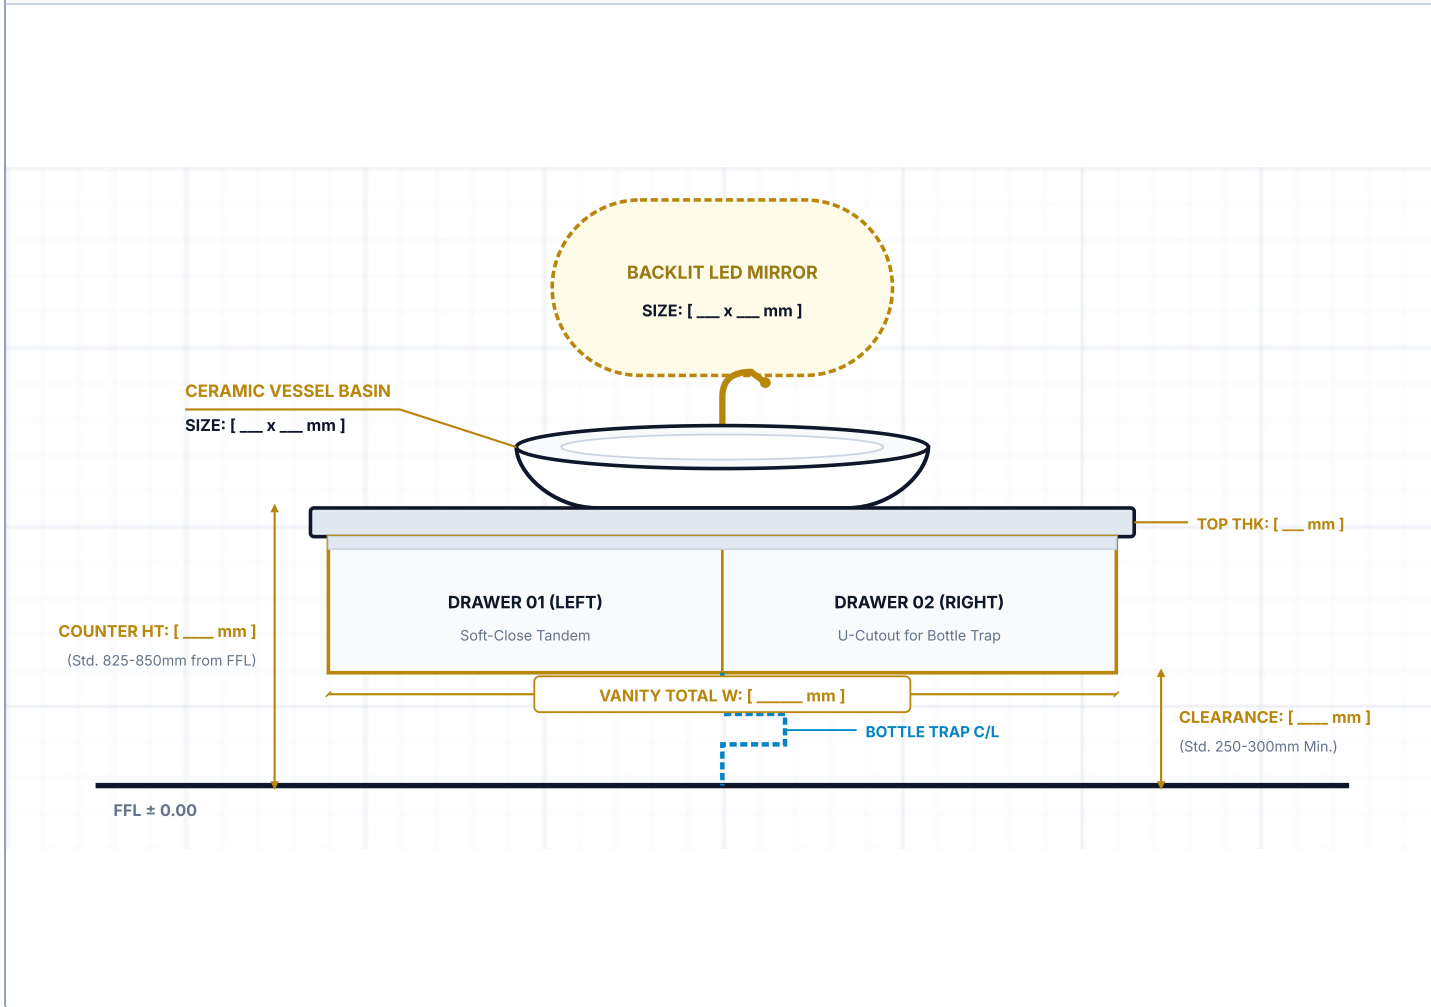

01 SANITARYWARE & BASIN DETAILS

WASHBASIN CONFIGURATION:

- | | |
|---|--|
| ☐ Table-Top Vessel Basin | ☐ Under-Counter Basin |
| ☐ Integrated Counter Basin | ☐ Wall-Hung Basin |

BASIN BRAND SELECTION:

- | | |
|--|--------------------------------|
| ☐ Kohler | ☐ Grohe |
| ☐ Jaquar Artize | ☐ Toto |

Basin Dimensions: [] x [] mm (Oval / Rect)

Countertop Stone: Quartz / Italian Marble / Granite

REMARKS: _____

02 VANITY CABINET & MIRROR

VANITY CABINET & MIRROR:

- | | |
|---|---|
| ☐ Wall-Mounted Floating Vanity | ☐ 2 Soft-Close Drawers |
| ☐ Open Shutter Ledge Below | ☐ Backlit Touch LED Mirror |
| ☐ Storage Mirror Medicine Box | ☐ Anti-Fog Demister Pad |

Countertop Height: 800 - 850 mm from FFL (Std. 32-34")

Faucet Specification: Tall Body Pillar Cock / Concealed Mixer

REMARKS: _____



PROJECT: _____

CLIENT: _____

SITE LOCATION: _____

DATE: _____

STATUS: SITE VERIFICATION

DWG 14-SHW

WASHROOM WET / DRY ZONING & SHOWER SECTION

SCALE: 1:25 • SECTIONAL ELEVATION • ALL DIMS BLANK FOR SITE ENTRY

10mm GLASS PARTITION: [____ x ____ mm]

DRY ZONE: WC AREA

FLUSH PLATE

HEALTH FAUCET

WALL-HUNG WC

CENTERLINE: [____ mm]

SEAT HT FROM FFL: [____ mm]

WET ZONE: SHOWER AREA

RAIN SHOWER: [____ mm]

LED NICHE
[____ x ____ mm]

DIVERTER: [____ mm]

SHOWER AREA: [____ (W) x ____ (L) ft]

SLOPE TO DRAIN (1:50)

01 WC & SHOWER SYSTEM

WATER CLOSET & CISTERN:

- | | |
|--|--|
| ☐ Rimless Wall-Hung WC | ☐ Floor-Mounted EWC |
| ☐ Smart Electronic Bidet WC | ☐ Concealed Cistern (Geberit) |
| ☐ Concealed Cistern (Grohe) | ☐ Concealed Cistern (Jaquar) |

SHOWER SYSTEM:

- | | |
|---|---|
| ☐ Concealed 3-Inlet Diverter | ☐ Overhead Rain Shower |
|---|---|

REMARKS: _____

02 GLASS ENCLOSURE & ACCESSORIES

GLASS ENCLOSURE & ACCESSORIES:

- | | |
|--|--|
| ☐ 10mm Toughened Glass Screen | ☐ Shower Niche with LED |
| ☐ Towel Rod (24") | ☐ Robe Hooks (Twin) |
| ☐ Toilet Paper Holder | ☐ Brass Health Faucet |

Fittings Brand & Series: Grohe / Kohler / Jaquar Artize

Hardware Finish Tone: Brushed Chrome / PVD Gold / Matt Black

REMARKS: _____



PROJECT: _____

CLIENT: _____

SITE LOCATION: _____

DATE: _____


STATUS: SITE VERIFICATION

DWG 15-MEP


PLUMBING RISER & ELECTRICAL INFRASTRUCTURE SCHEMATIC

SCALE: 1:20 • MEP SCHEMATIC • ALL DIMS BLANK FOR SITE ENTRY

A. PLUMBING RISER & GEYSER DETAIL

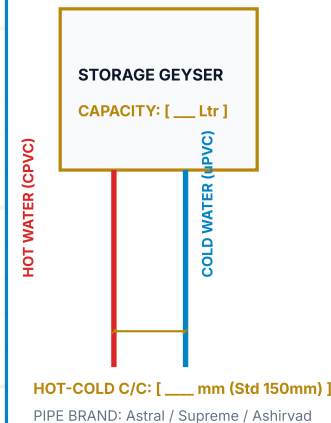

B. ELECTRICAL CONDUIT & DB LAYOUT

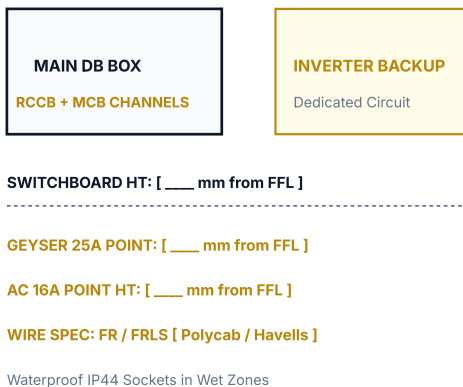

01 PLUMBING & PIPING SPECIFICATIONS

PLUMBING & DRAINAGE:

- | | |
|--|--|
| ☐ Astral CPVC / Supreme | ☐ Ashirvad FlowGuard |
| ☐ uPVC SWR Drainage Pipes | ☐ Linear Trench Drain |
| ☐ Normal Gravity Flow | ☐ Pressure Booster Pump |

Hot & Cold Center-to-Center: Strict 150 mm Center Distance (Std)

REMARKS: _____

02 ELECTRICAL WIRING & POWER POINTS

ELECTRICAL WIRING & SWITCHES:

- | | |
|---|--|
| ☐ Finolex FRLS Wiring | ☐ Polycab Fire-Resistant |
| ☐ Schneider Zencelo Switches | ☐ Legrand Arteor Switches |

Geyser Point (25A): 84" from FFL (Inside False Ceiling / Loft)

Waterproof Sockets: Shaver Socket + Hairdryer (Dry Vanity)


REMARKS: _____



PROJECT: CLIENT: SITE LOCATION: DATE: STATUS: SITE VERIFICATION

DWG 16-RCP REFLECTED CEILING PLAN (RCP) & COVE LIGHTING SECTION

SCALE: 1:30 • REFLECTED CEILING PLAN • ALL DIMS BLANK FOR SITE ENTRY

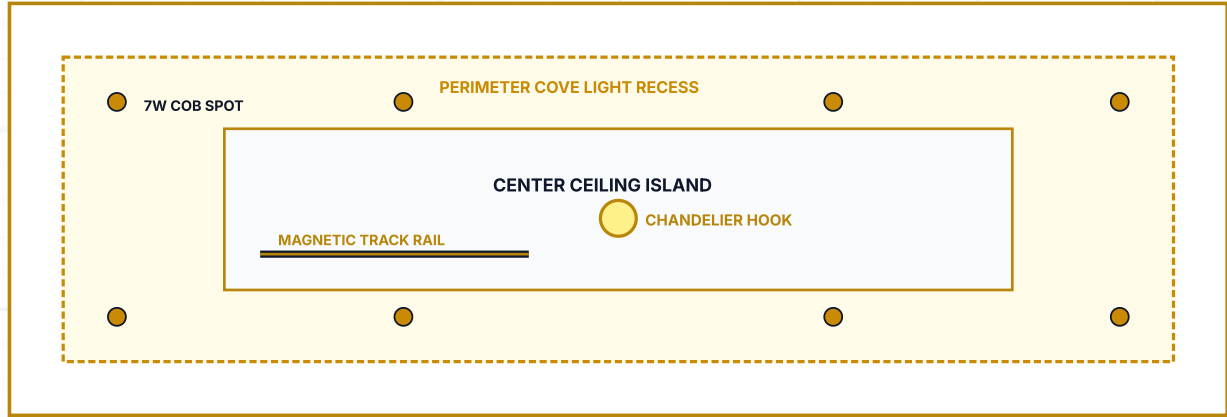

TYPICAL COVE SECTION DETAIL:

COVE DROP: [] mm • COVE POCKET LIP: [] mm • CLEAR HT: [] ft

LED STRIP (3000K)

01 CEILING MATERIAL & COVE ARCHITECTURE

CEILING COVERAGE & MATERIAL:

- ☐ Entire Home Ceiling Drop ☐ Living & Dining Only
☐ Bedrooms Only ☐ Moisture Board in Baths
☐ Saint-Gobain Gyproc 12.5mm ☐ POP Plaster Ceiling

COVE LIGHTING SYSTEM:

- ☐ Perimeter Cove Strip ☐ Curtain Pelmet Cove

REMARKS:

02 FIXTURE SELECTION & VENTILATION

LIGHTING FIXTURE SELECTION:

- ☐ Recessed Anti-Glare COB Spots ☐ Magnetic Track Lights
☐ Surface Cylinder Spots ☐ Chandelier Center Point
☐ Warm White Strip (3000K) ☐ Neutral Day Strip (4000K)

Ceiling Paint Specification: Asian Paints Royale / Matte White

Ventilation / Exhaust Cutouts: Washroom Exhaust & Chimney Duct

REMARKS:



PROJECT: _____

CLIENT: _____

SITE LOCATION: _____

DATE: _____


STATUS: SITE VERIFICATION

DWG 17-OPN


DOORS, WINDOWS & BALCONY RAILING ARCHITECTURAL DETAIL

SCALE: 1:20 • 2D ELEVATION • ALL DIMS BLANK FOR SITE ENTRY


1. MAIN ENTRANCE DOOR

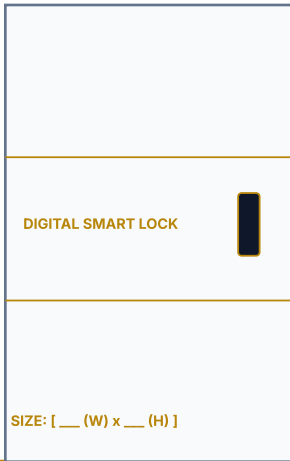

2. 3-TRACK SLIDING WINDOW

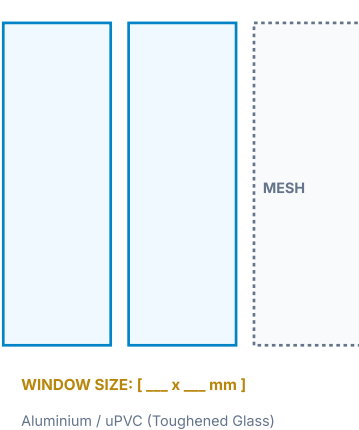

3. BALCONY GLASS RAILING

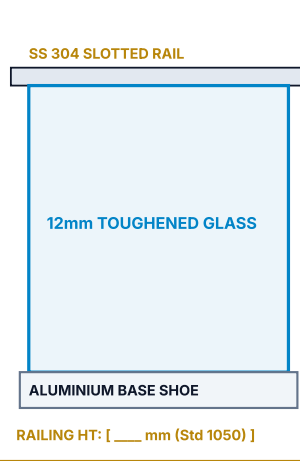

01 MAIN & INTERNAL DOORS

MAIN & INTERNAL DOORS:

- | | |
|--|--|
| ☐ Solid Teak Wood Door | ☐ Teak Veneer Skin Door |
| ☐ CNC Metal Grill Safety Door | ☐ Yale Biometric Smart Lock |
| ☐ Solid Core Flush (32mm) | ☐ Veneer with Architrave |

REMARKS: _____

02 WINDOWS & BALCONY RAILINGS

WINDOWS & BALCONY RAILINGS:

- | | |
|--|---|
| ☐ uPVC 3-Track Sliding Window | ☐ Aluminium Slim Profile |
| ☐ Toughened Double Glazing | ☐ 12mm Glass Balcony Railing |
| ☐ SS 304 Spigots & Handrail | ☐ Laser Cut MS Grill Railing |

Door Hardware & Hinges: SS 304 Ball Bearing Hinges + Stops

Hardware Finish Tone: Brushed SS / Antique Brass / Black

REMARKS: _____




PROJECT: _____ CLIENT: _____ SITE LOCATION: _____ DATE: _____ STATUS: SITE VERIFICATION

DWG 18-APV

SPECIAL FEATURES ELEVATION & OFFICIAL APPROVAL TITLE BLOCK

SCALE: 1:20 • APPROVAL SHEET • ALL DIMS BLANK FOR SITE ENTRY

A. POOJA / MANDIR UNIT

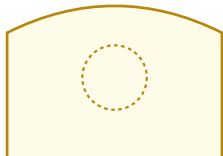

CNC BACKLIT JALI

SIZE: [_ x _ x _ mm]

B. HOME BAR COUNTER

WINE STEMWARE RACK

QUARTZ SERVICE LEDGE

BAR W: [_ mm] • HT: [_ mm]

C. SMART HOME AUTOMATION

CENTRAL IOT GATEWAY

• Smart Curtain Motors (W: _)

• 4-Scene Mood Lighting

• Digital Biometric Door Lock

PROTOCOL: Zigbee / Matter

INTERIOR DESIGNER SIGN-OFF

Lead Architect / Designer:

SIGNATURE & DATE

SITE PROJECT ENGINEER

Site Verification & Civil Check:

SIGNATURE & DATE

CLIENT APPROVAL & SIGN-OFF

Final Specification Acceptance:

CLIENT SIGNATURE & DATE

01 BESPOKE UNITS & AUTOMATION

BESPOKE FEATURE UNITS:

- ☐ Pooja / Mandir Unit (CNC Backlit) ☐ Home Bar Counter Unit
☐ Balcony Sit-Out Deck ☐ Home Theater Acoustic Paneling

SMART HOME AUTOMATION:

- ☐ Smart Curtain Motors ☐ App/Voice Mood Lighting
☐ Digital Motion Sensors ☐ Central Smart Gateway

REMARKS: _____

02 PROJECT BUDGET & FINAL CLIENT APPROVAL

BUDGET & SCOPE AGREEMENT:

- ☐ Strict Fixed Budget ☐ Up to 10% Scope Flexibility
☐ Phase-wise Execution ☐ Turnkey Studio Sign-off

Estimated Project Budget: Rs. [_____]

Target Handover Date: DD / MM / YYYY (____ Days)

Special Studio Directives: Strict QA Inspection & Material Sign-off

REMARKS: _____